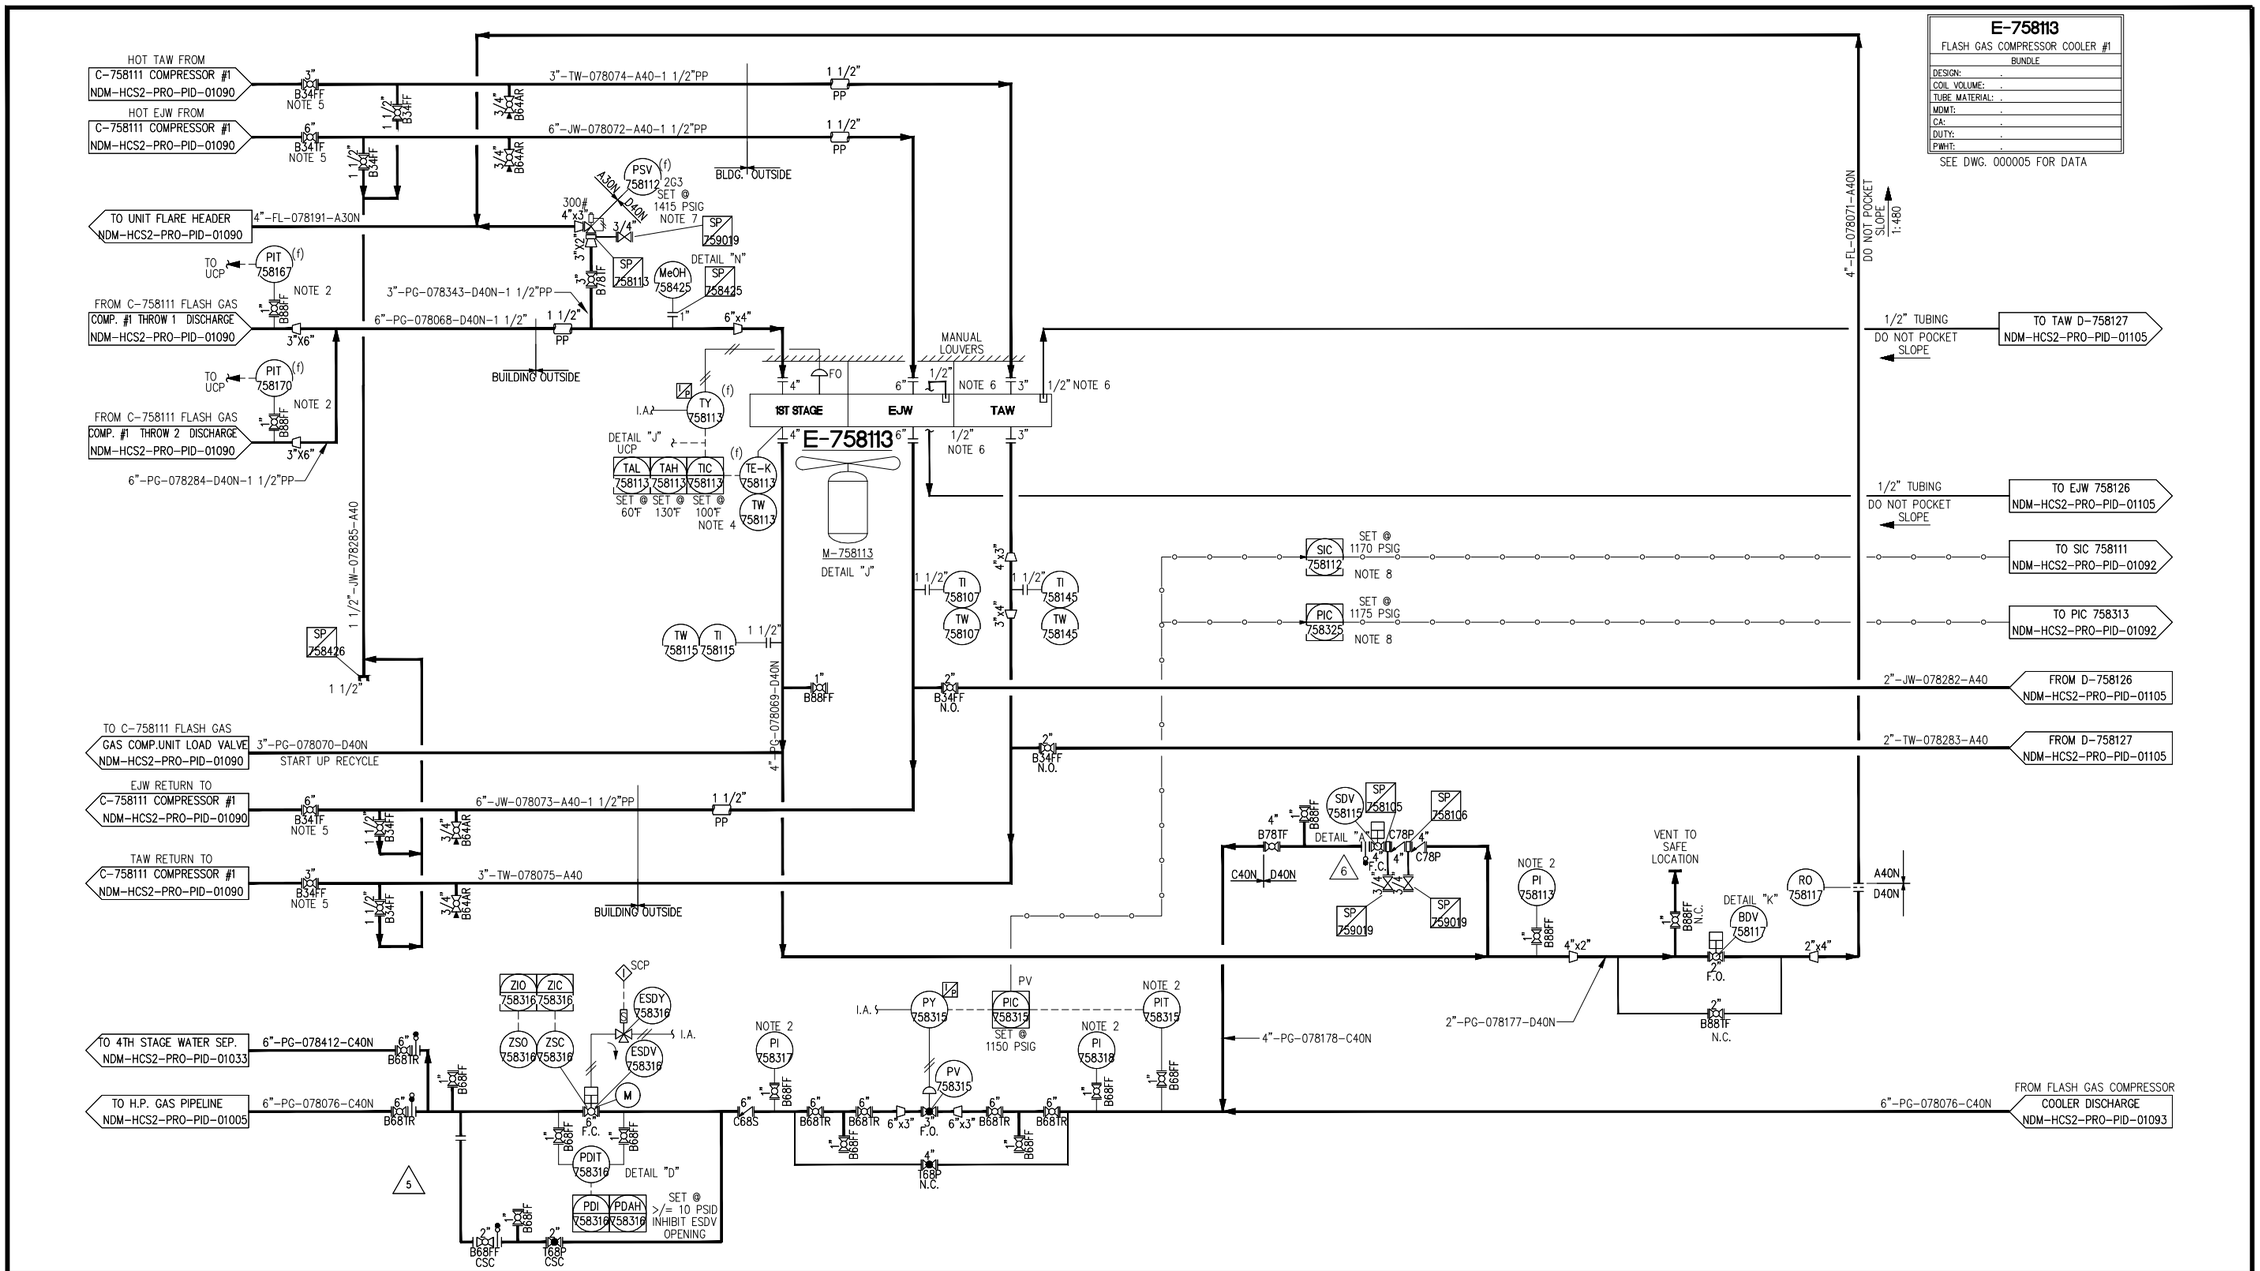

NOTES:
1. DELETED.
2. SEE DETAIL "L" FOR CONFIGURATION.
3. DELETED.
4. TE-K AND TW WILL BE ON NOZZLE @ 45° WITH 3/4" NPT TAP FOR TW.
5. VALVE TO BE LOCATED NEAR COMPRESSOR.
6. HIGHEST TUBE PLUG.
7. PSV IS HEAT TRACED AND INSULATED AND BONNET TO BE COVERED BY INSULATION JACKET.
8. FOR DISCHARGE CONTROL, SEE NDP-HCS-INS-RPT-000-STA-000001.

(f) = FURNISHED BY VENDOR.

REVISIONS

NO	DATE	DESCRIPTION	DRAWN BY	CHK'D BY	APPV'D BY
5	09/24/18	ISSUED FOR CONSTRUCTION (WOP NDM-HCS2-MUD-WOP-01001)	SJM	CR	GG
4C	07/27/18	ISSUED FOR DESIGN (WOP NDM-HCS2-MUD-WOP-01001)	SJM	CR	GG
4B	07/05/18	ISSUED FOR APPROVAL (WOP NDM-HCS2-MUD-WOP-01001)	SJM	CR	GG
4A	05/23/18	ISSUED FOR REVIEW	LRM	CR	GG
4	02/08/18	ASBUILT – HESS DOCUMENT NUMBER UPDATE	S.M	JLG	JLG
3	02/16/17	FOR THE RECORD UPDATE	DS	MS	MS
2	04/11/16	ISSUED FOR CONSTRUCTION	LC	DS	MH
1	10/29/15	ISSUED FOR CONSTRUCTION	XYM	RZJ	DR
6	06/22	REVISED PER MOC # MOC-2022-00252	AN	CR	CR

HESS CORPORATION
EXPLORATION & PRODUCTION

NORTH DAKOTA MIDSTREAM

HAWKEYE COMPRESSOR STATION

PIPING & INSTRUMENTATION DIAGRAM
FLASH GAS COMPRESSOR COOLER #1

DRAWN BY: SJH	DESGN BY:	CHECKED BY:	APPRVD BY:	DATE: 6/11/14	SCALE:

SIZE	DRAWING No.	HESS DRAWING No.	REV
D	NDP-HCS-PRO-PID-078-STA-078011	NDM-HCS2-PRO-PID-01091	6

UNCONTROLLED WHEN PRINTED